



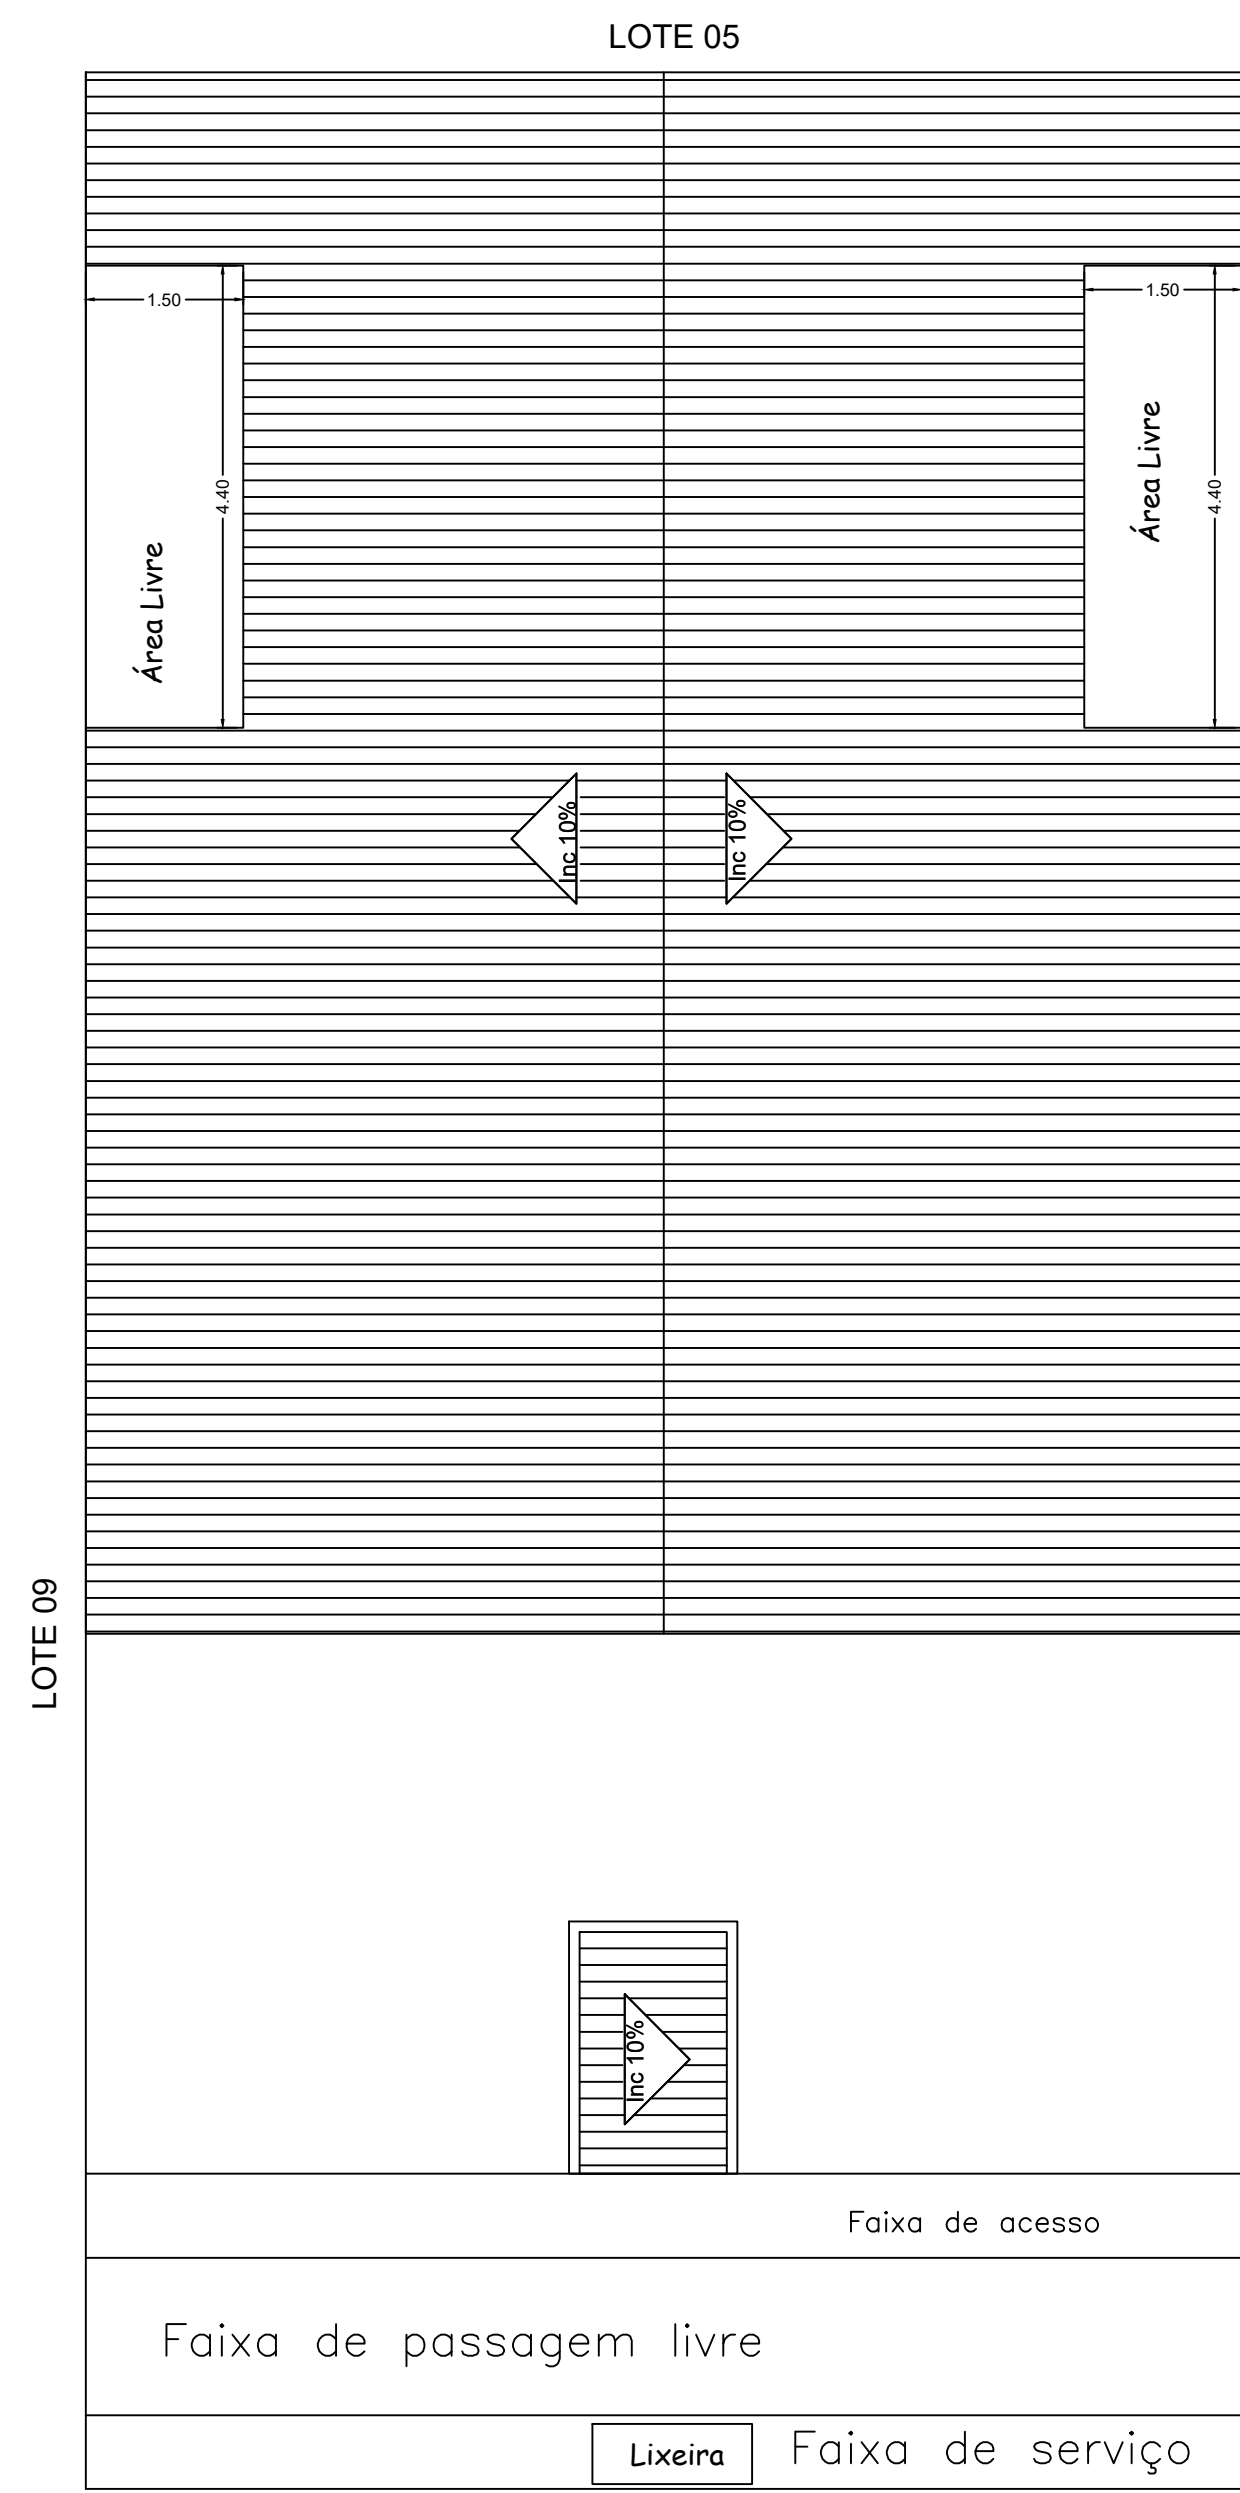

Cobertura

RUA ADRIANO CINTRA - VOL.


Esc. 1/100

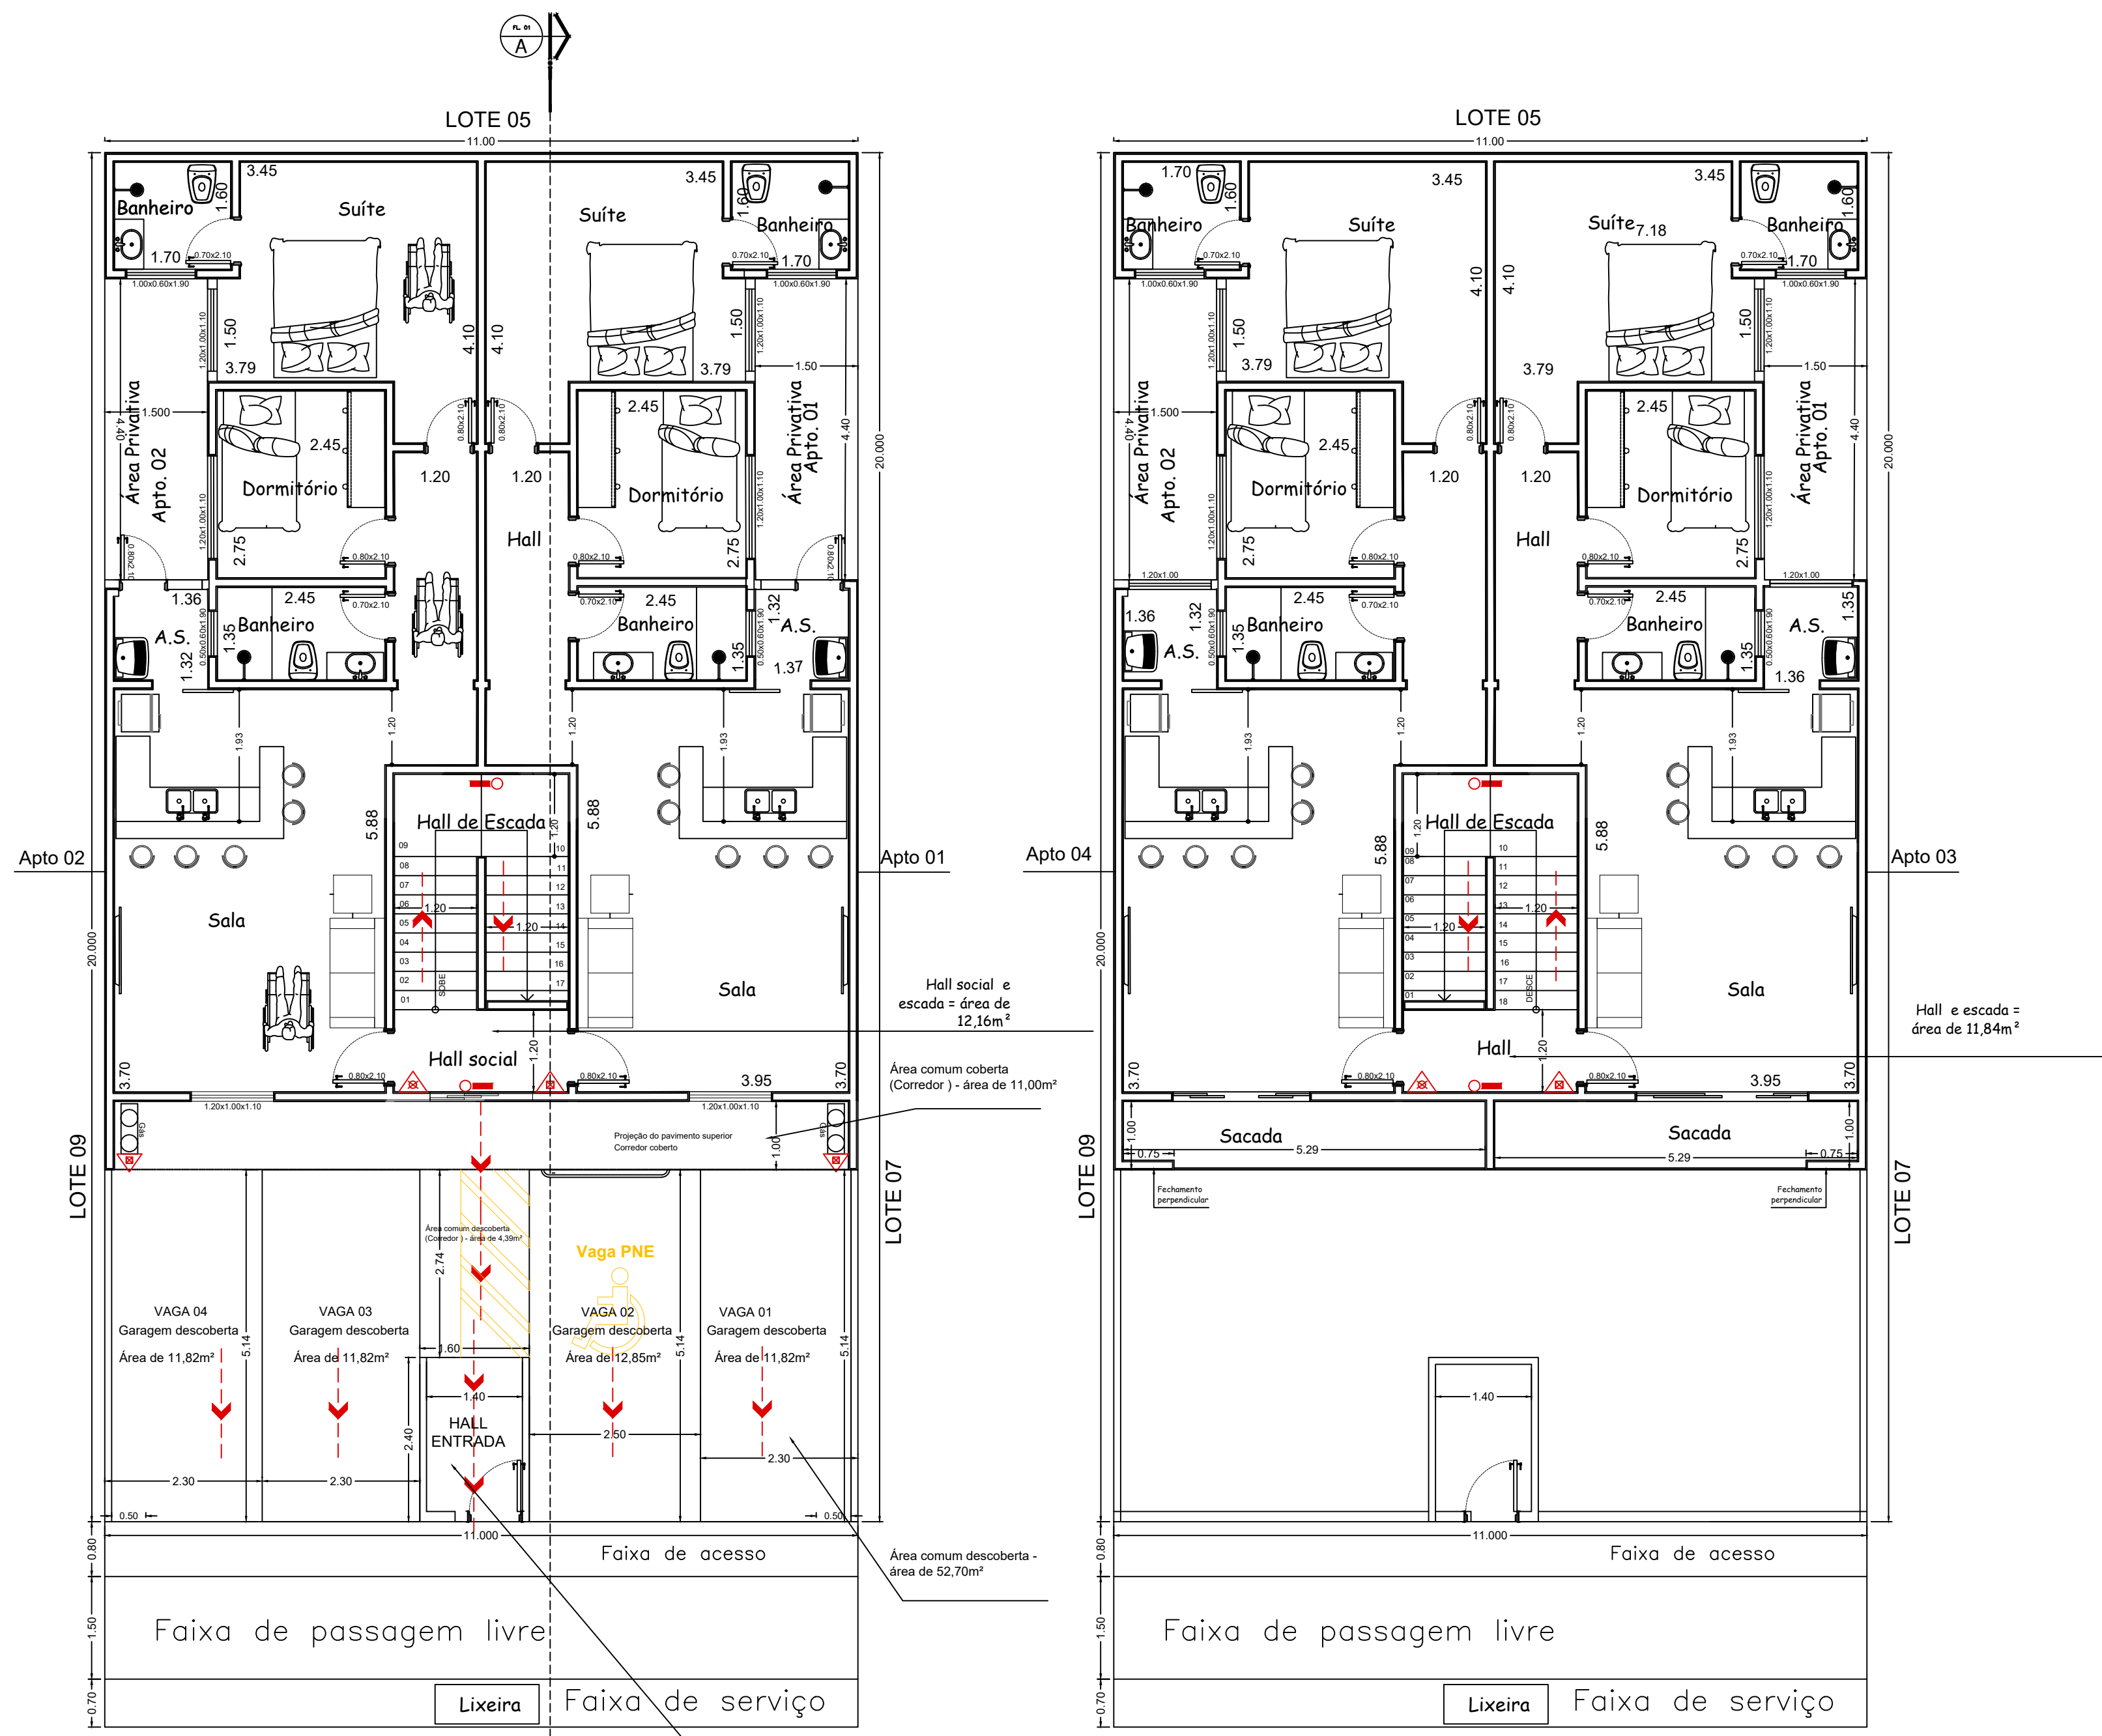

Planta 1º Pav. Terreo

RUA ADRIANO CINTRA - VOL.

Esc. 1/100

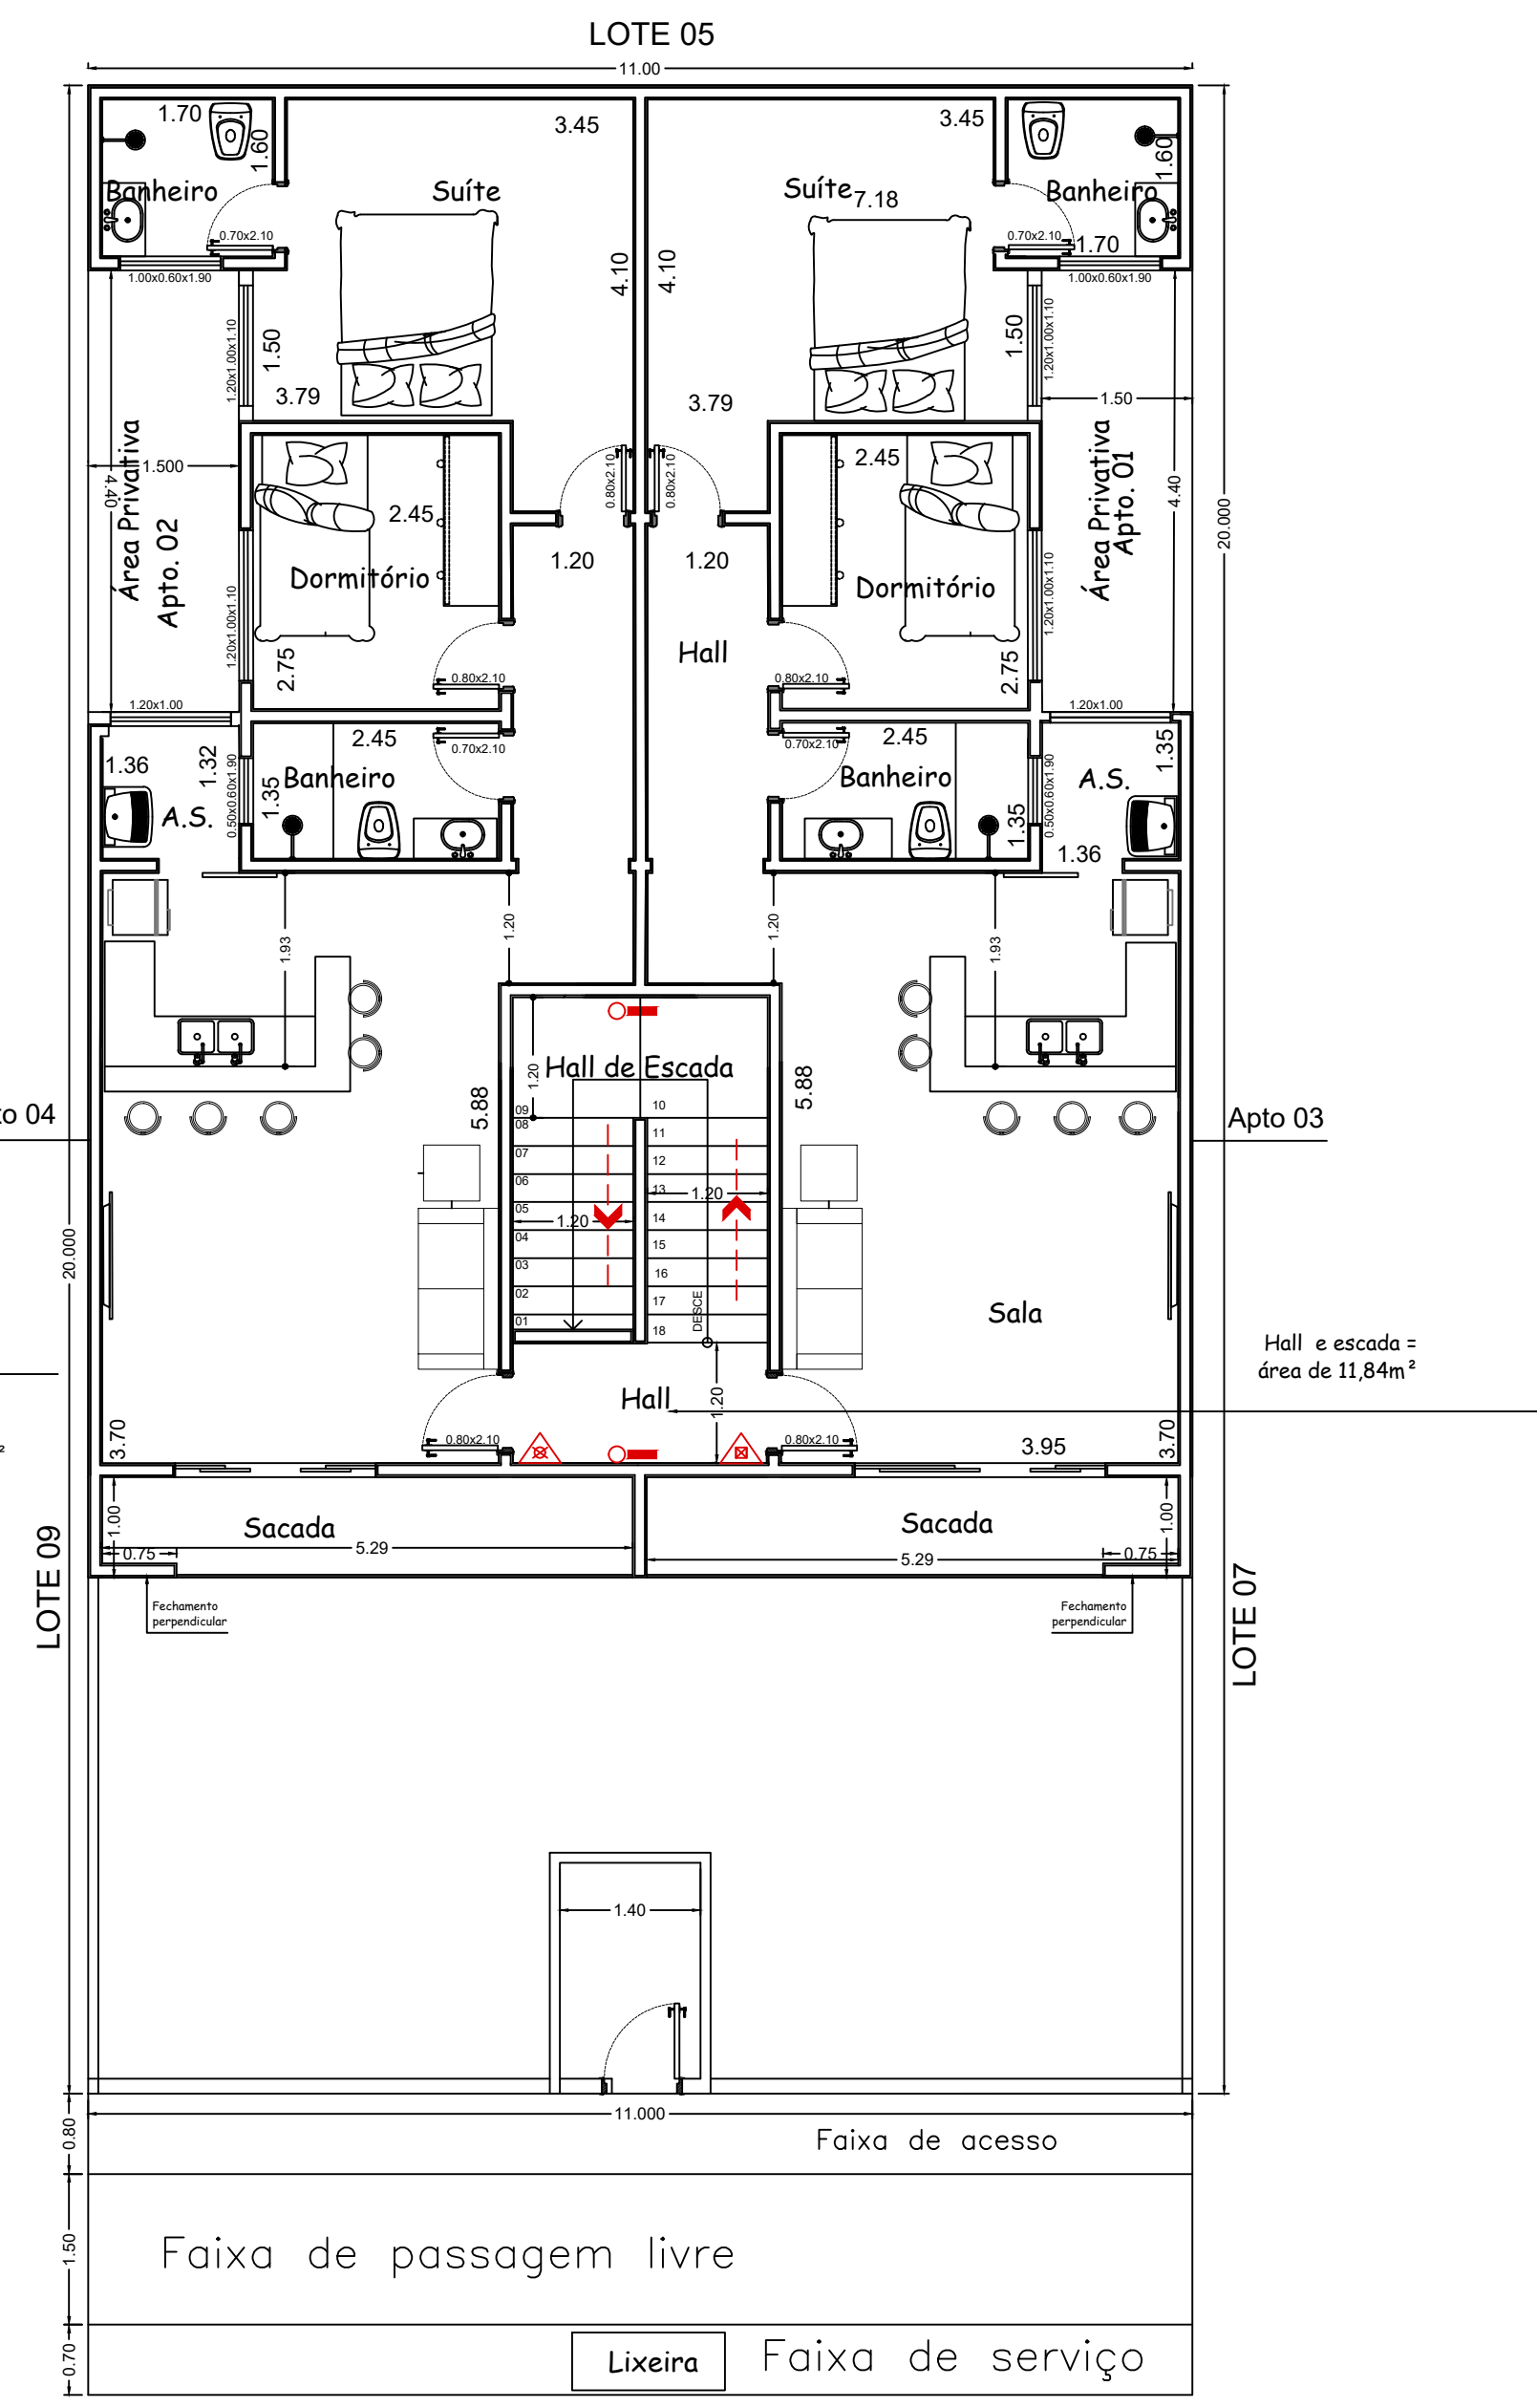

Planta 2º Pav. 1º Andar


RUA ADRIANO CINTRA - VOL.

Esc. 1/100

LEGENDA DE SISTEMA DE SEGURANÇA	
	CARGA DE PÓ 20 - B-C
	CARGA D'ÁGUA 2 - A
	PONTO DE ILUMINAÇÃO DE EMERGÊNCIA (ACLARAMENTO)
	CHAVE ELÉTRICA PRINCIPAL
	DIREÇÃO DO FLUXO DE ROTA DE FUGA
	SAÍDA FINAL DE ROTA DE FUGA


QUADRO DE ÁREAS DE PROJETO

APTº	ÁREA UTIL M²	ÁREA COMUM COBERTA (HALLS, ESCADAS e Corredores)	ÁREA PRIVATIVA DESCOBERTA	ÁREA CONSTRUIDA TOTAL	ÁREA Comum Descoberta	ÁREA TOTAL CONSTRUIDA e DESCOBERTA
01	63,55	9,71	6,60	73,26	13,1750	93,0350
02	63,55	9,71	6,60	73,26	13,1750	93,0350
03	69,06	9,71	----	78,77	13,1750	91,9450
04	69,06	9,71	----	78,77	13,1750	91,9450
	265,22	38,84	13,20	304,06	52,7000	369,9600

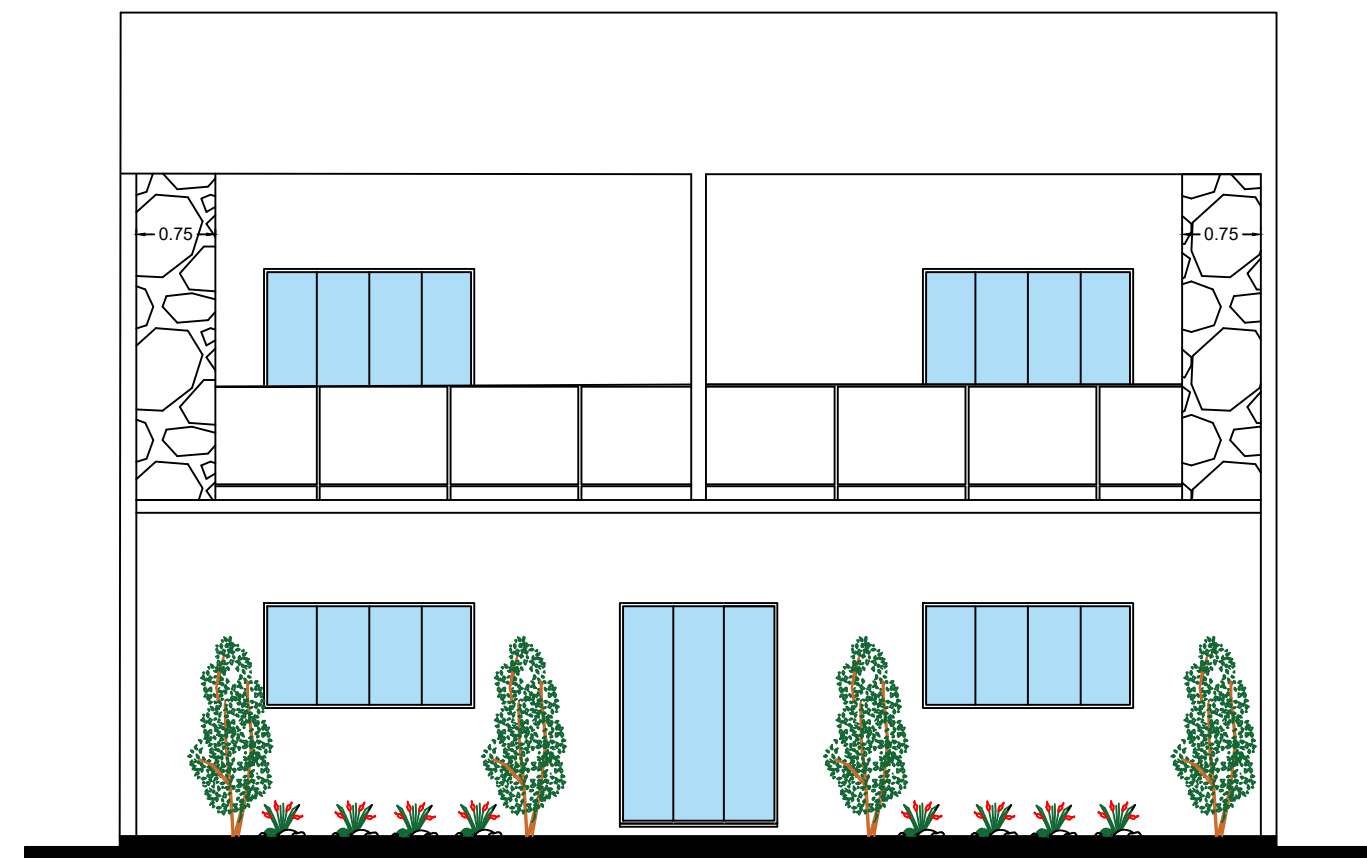

Elevação


Esc. 1/100

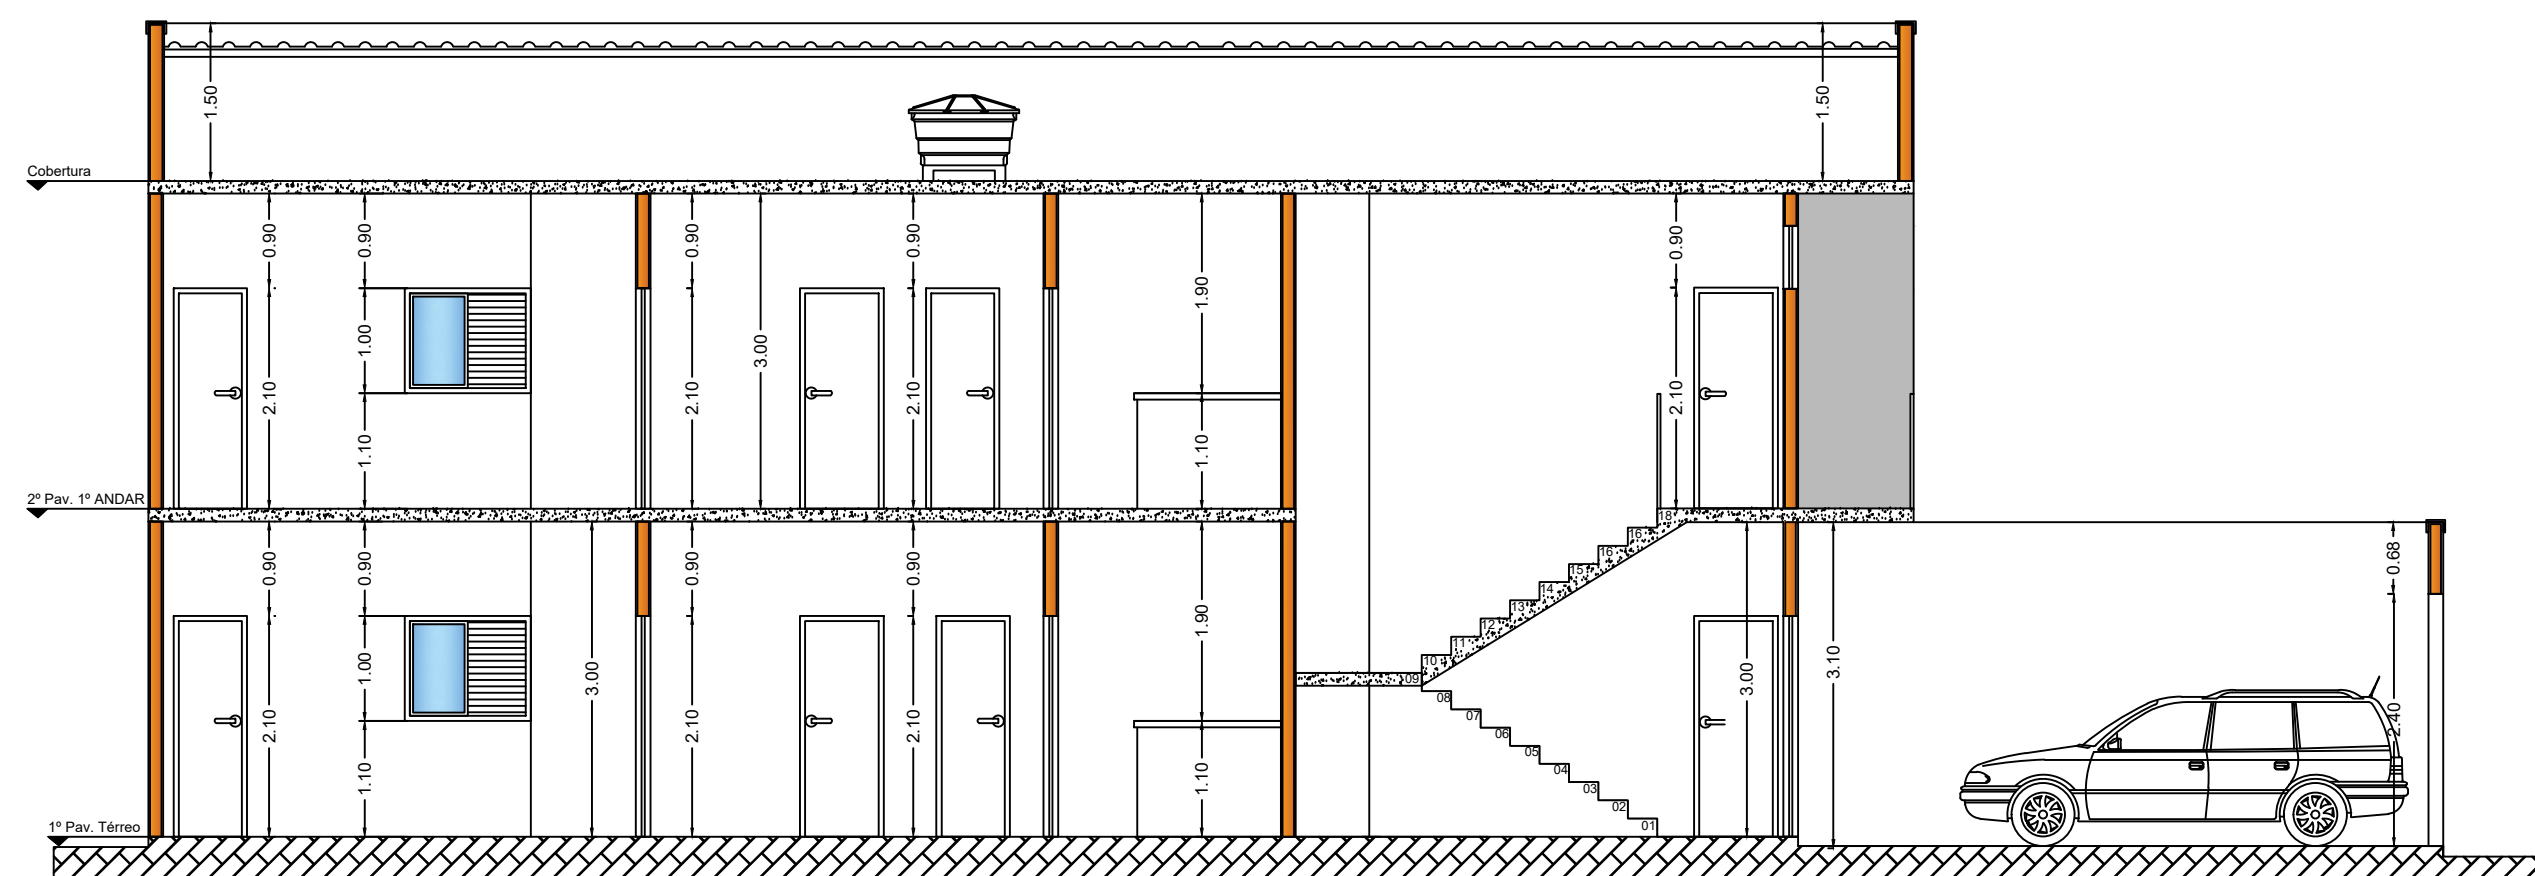

Corte A-A

Esc. 1/100

Cunha de Acesso

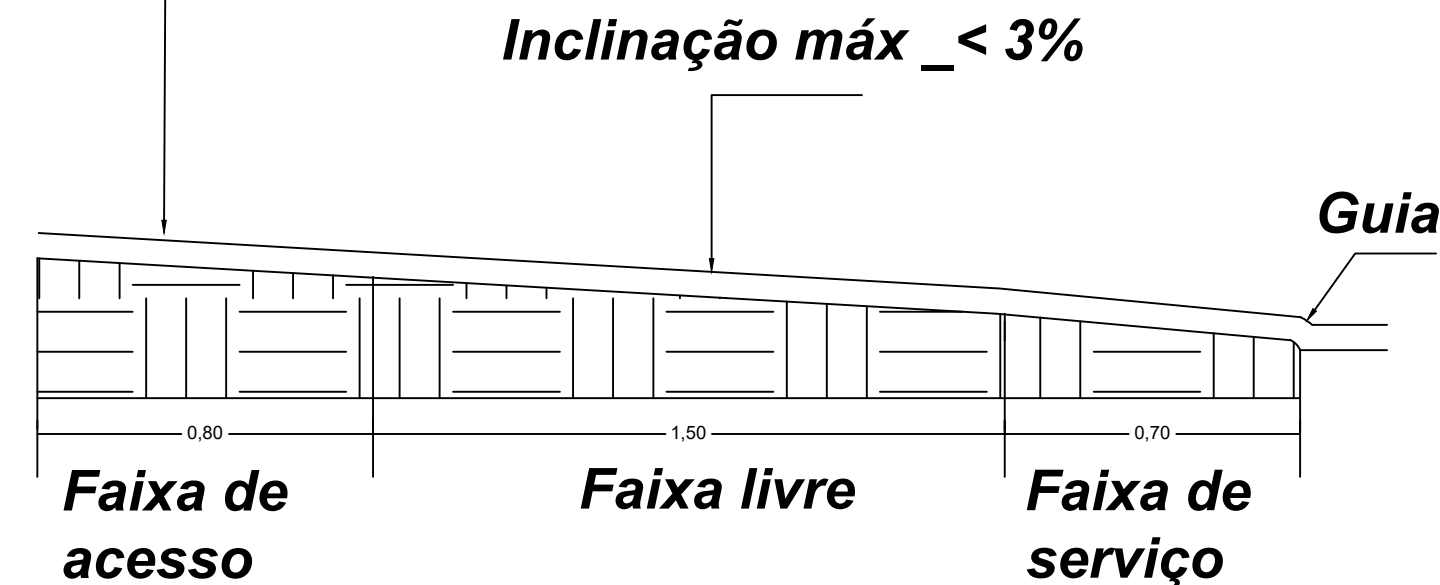

Corte Transversal ESCALA :: 1:50


Inclinação máx _< 3%

Guia


Faixa de
acesso

Faixa livre

Faixa de
serviço

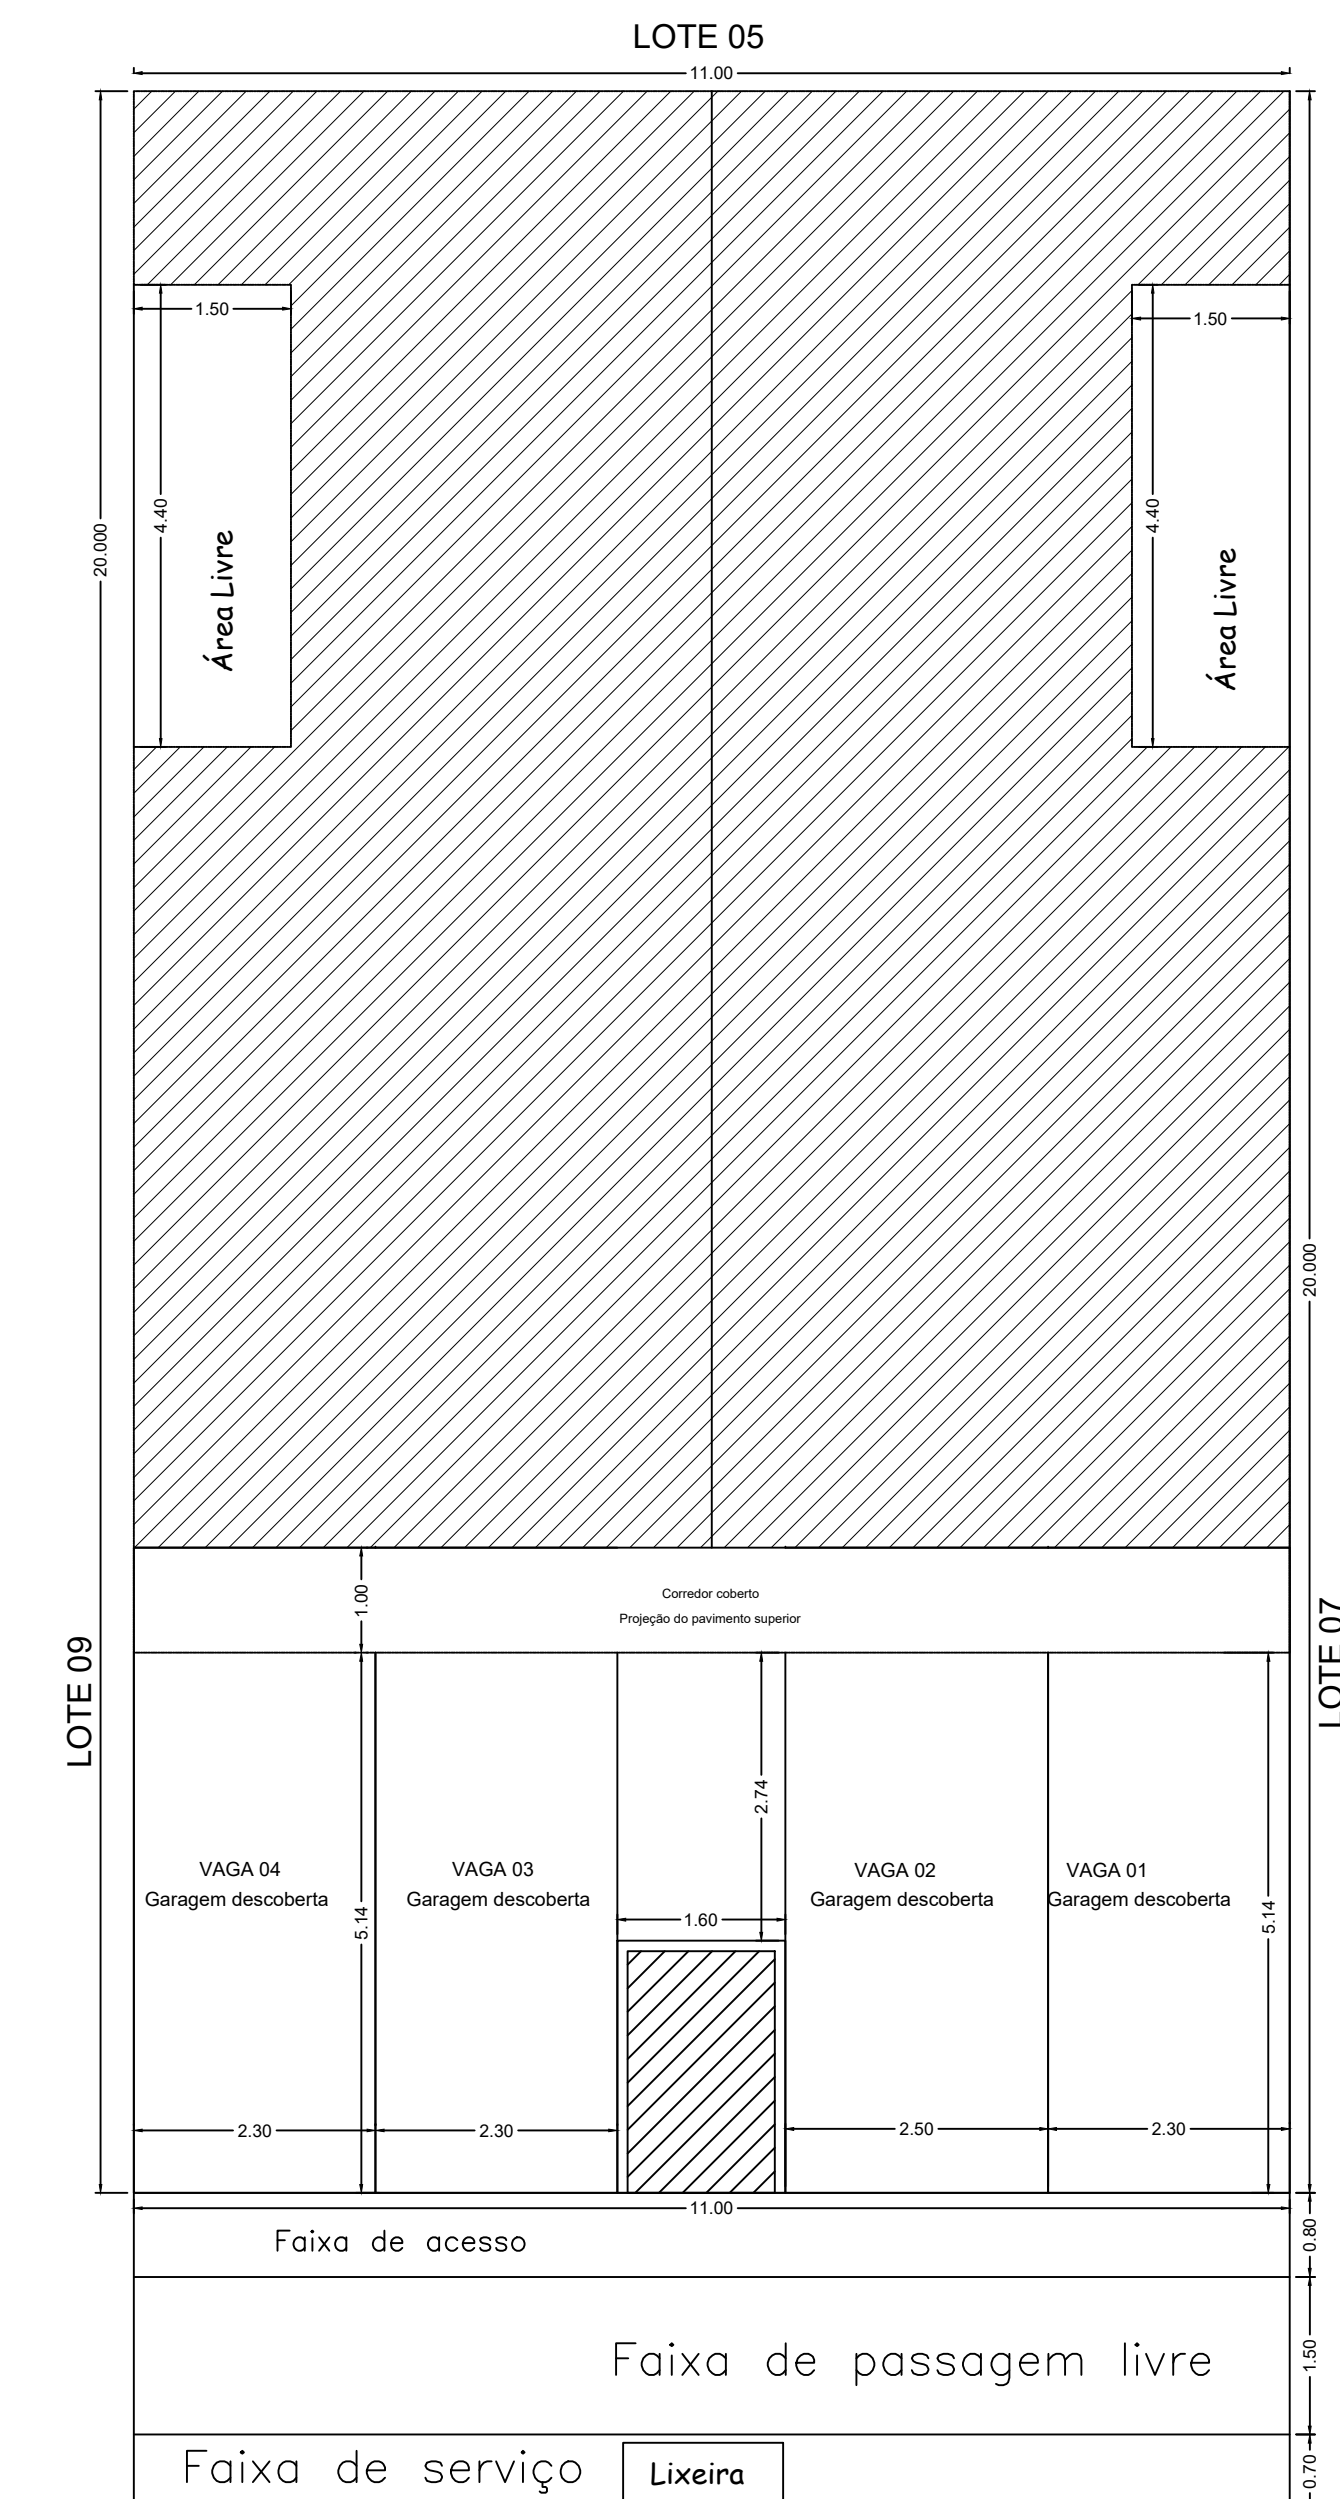


Implantação 1º Pav. Térreo

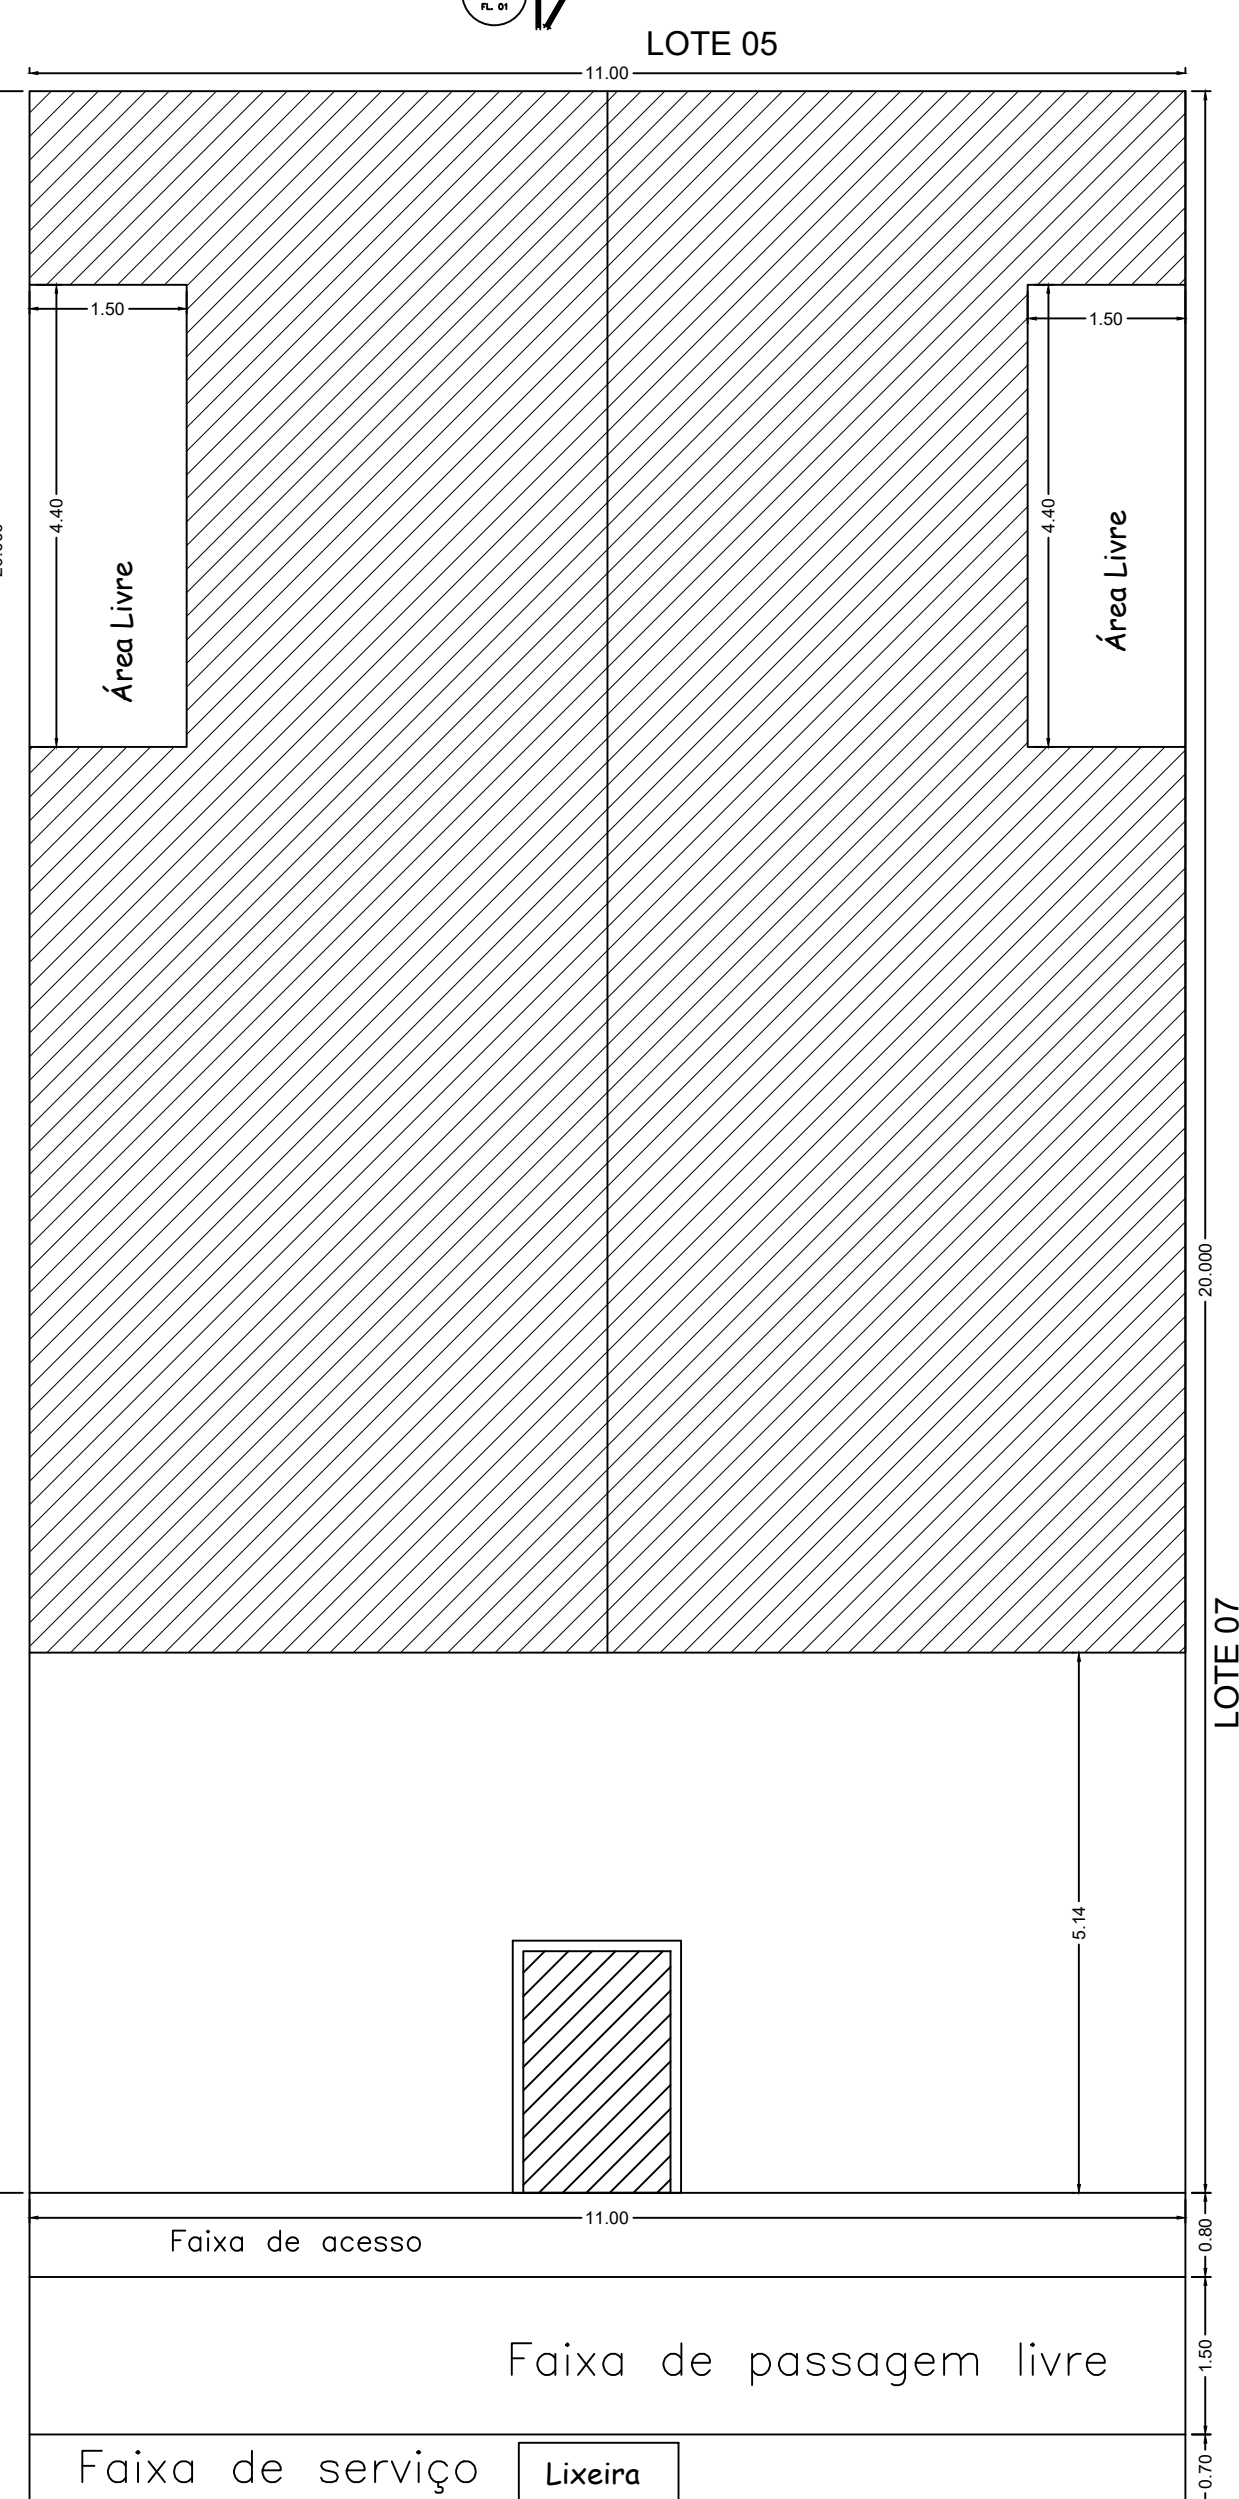

Implantação 2º Pav. 1º Andar

RUA ADRIANO CINTRA - VOL.

LOCALIZAÇÃO

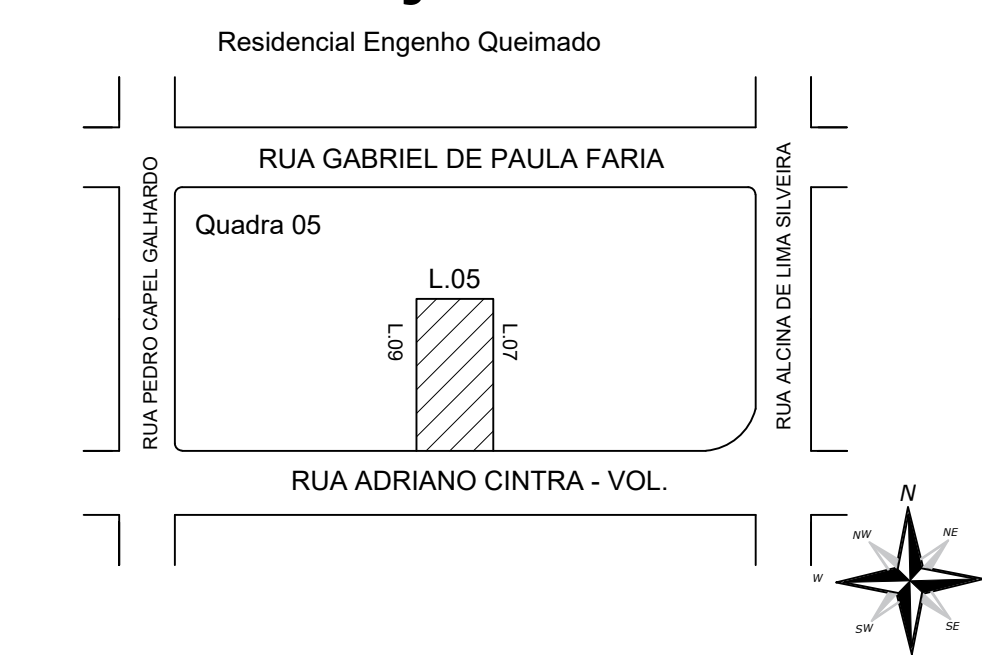

Número do Protocolo	Cód. Verificador	Título	Data de deferimento
2025MF0076	1ah0eah4	2025MF0076	3 de novembro de 2025.

Título do processo
Projeto de Regularização de Residencial Multifamiliar submetido à Lei Federal 4591/64 - Nome do
condomínio: RESIDENCIAL SGARIONI

Proprietário	CPF/CNPJ do Proprietário
YGOR MARANGONI SGARIONI	387.***.***-81

Responsável Técnico	Responsabilidade	Conselho	ART
DANILO MAGNANI	Projeto	5069490727	2620251604418
Responsável Técnico	Responsabilidade	Conselho	ART
LAZARO THOME DA SILVA NETO	Execução	5070668785	2620251877245

Cadastro do Imóvel	Endereço	Número
01.1.13.04.015.08.00	RUA ADRIANO CINTRA - VOL.	1890
Localização do imóvel	Lot	Quadra
RESIDENCIAL ENGENHO QUEIMADO	08	5

Tip de uso	Área total, por tipo de uso	Área aprovada
Residencial Multifamiliar	304,06 m²	0 m²
Área a ser construída (aprovada)	0 m²	Área a ser demolida (aprovada)
0 m²	304,06 m²	0 m²

Área do terreno	Total de área verificada	Total de área a construir	Total de área a regularizar	Área total do imóvel
220,00 m²	0,00 m²	0,00 m²	304,06 m²	304,06 m²

Taxa de Ocupação	Área Total Permissível	Área Total Impermissível	Taxa de Permissibilidade	Número de pavimentos
70,05 %	0,00 m²	220,00 m²	0,00 %	2

PREFEITURA MUNICIPAL DE FRANCA
SECRETARIA MUNICIPAL DE
INFRAESTRUTURA
SETOR DE APROVAÇÃO DE PROJETOS

Licenciado por

Analista de Projetos

Nome

Camila Cardoso (Aprovação de Projetos)

Deferido por:

Enio Domingues (Aprovação de Projetos)

Cargo:

Analista de Projetos, Diretoria

Franca, 3 de novembro de 2025.